

FLOOR PLAN GENERAL NOTES

- ALL DIMENSIONS ARE TO THE FACE OF FINISH U.N.O.
- FOR UNIT PLANS SEE SHEETS A5-101 THROUGH A5-110
- FOR WALL PARTITION TYPES SEE SHEET A5-101
- FOR DOORS SEE SCHEDULES ON SHEET A5-101
- FOR WINDOWS & LOUVERS SEE SCHEDULES ON SHEET A5-101
- FOR BOH FINISHES SEE SHEET A5-01
- REFER TO SHEET A5-025 THROUGH A5-033 FOR ACCESSIBILITY REQUIREMENTS FOR ACCESS AND CLEARANCES
- WALL RATING LINES ARE INTENDED TO SHOW OCCUPANCY SEPARATIONS ONLY. REFER TO LIFE SAFETY CODE FOR REQUIRED RATINGS OF VARIOUS BUILDING ELEMENTS.
- ELEVATOR DOORS IN 2 HOUR SHAFT WALLS SHALL BE RATED 90 MINUTES
- CONDUIT FOR COUNTRYWIDE COORDINATED CONDUIT SYSTEM TO BE LOCATED IN CEILING. RUN CONDUIT VERTICALLY THROUGH CTY ROOM ON ALL UPPER LEVELS.

FLOOR PLAN LEGEND

	CONCRETE MASONRY
	CONCRETE COLUMNS & SHEAR WALLS
	INDICATES 1 HR RATED ASSEMBLY PER WALL TYPE
	INDICATES 2 HR RATED ASSEMBLY PER WALL TYPE
	PROPERTY LINE
	FLOOR DRAIN - SEE PLUMBING DWGS
	FLOOR SINK - SEE PLUMBING DWGS
	SLOPE ARROW, SLOPE 1/8" FT @ INTERIOR & 1/4" FT @ EXTERIOR SPACES U.N.O.

ELECTRICAL SYMBOLS

	INTERIOR WALL TYPE PER SHEET A9-001
	SEE SIGNAGE KEYNOTE LEGEND
	WALL MOUNTED DECORATIVE SCONCE, PER INTERIOR DWGS
	SEMI-RECESS FIRE EXTINGUISHER CABINET, A9-002
	SURFACE MOUNTED FIRE EXTINGUISHER
	STANDPIPE LOCATION, REFER TO FIRE SPRINKLER DWGS & APPROVED FIRE MASTER PLAN
	POWER OUTLET, MOUNTED @ 18" AFF U.N.O. (SEE ELEC. DWGS)
	POWER OUTLET, RECESSED IN FLOOR, PROVIDE POWER, DATA & TV (SEE ELEC. DWGS)
	COMBO OUTLET, RECESSED IN FLOOR, PROVIDE POWER, DATA & TV (SEE ELEC. DWGS)
	INSTALL TV OUTLET AT BACK OF TV. (HEIGHT PER INTERIOR DWGS)
	TELE/DATA OUTLET, MOUNTED @ 18" AFF U.N.O. (ELEC. DWGS)
	DATA OUTLET, MOUNTED @ 18" AFF U.N.O. (ELEC. DWGS)
	SWITCH, MOUNTED @ 48" AFF U.N.O. (ELEC. DWGS)
	HOUSE PHONE, WALL MOUNTED @ 48" AFF U.N.O. (T.O. PHONE) - PROVIDE RECEPTACLE FOR CONNECTION

KEYNOTES / LEGENDS

KEYNOTE LEGEND	
	TACTILE FLOOR LEVEL IDENTIFICATION SIGNAGE, MOUNT AT 60" AFF TO CENTERLINE OF SIGNAGE
	STARWELL IDENTIFICATION SIGNAGE PER DTL 24080020

WATG

strategy planning architecture landscape interiors

irvine | CA | 949 574 8500 watg.com




THE LITTLE NELL
HOTEL GROUP

client | consultant



stamp | approval

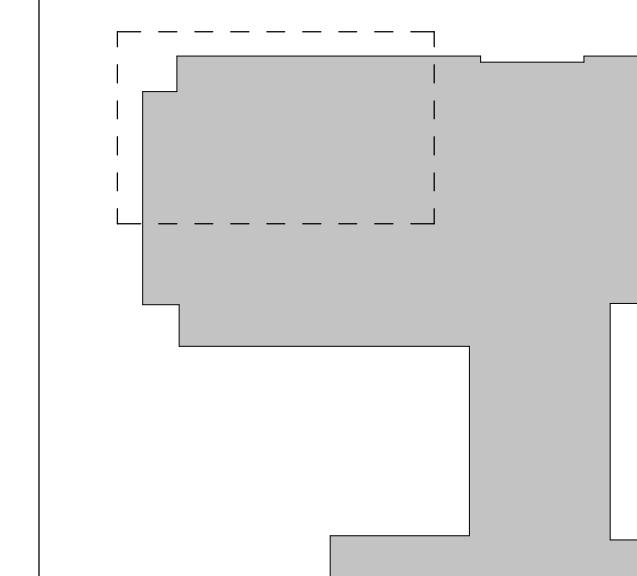

key plan



LIMELIGHT HOTEL

1295 UNIVERSITY AVE BOULDER, CO 80302
CU PROJECT NO. - UCB000740 - CCH

project logo

FLOOR PLAN - LEVEL 1 - SECTOR 1A

sheet title

project no. 214013

date 12/07/22

checked by: Checker

drawn by: Author

HT component


sheet no.

A2-105


FLOOR PLAN GENERAL NOTES

- ALL DIMENSIONS ARE TO THE FACE OF FINISH U.N.O.
- FOR UNIT PLANS SEE SHEETS A5-101 THROUGH A5-110
- FOR WALL PARTITION TYPES SEE SHEET A5-101
- FOR DOORS SEE SCHEDULES ON SHEET A10-101
- FOR WINDOWS & LOUVERS SEE SCHEDULES ON SHEET A10-101
- FOR BOH FINISHES SEE SHEET A10-01
- REFER TO SHEET A0-025 THROUGH A0-033 FOR ACCESSIBILITY REQUIREMENTS FOR ACCESS AND CLEARANCE
- WALL RATING LINES ARE INTENDED TO SHOW OCCUPANCY SEPARATIONS ONLY. REFER TO LIFE SAFETY DRAFT FOR REQUIRED RATINGS OF VARIOUS BUILDING ELEMENTS.
- ELEVATOR DOORS IN 2 HOUR SHAFT WALLS SHALL BE RATED 90 MINUTES
- CONDUIT FOR COUNTRYWIDE COORDINATED CONDUIT SYSTEM TO BE LOCATED IN CEILING. RUN CONDUIT VERTICALLY THROUGH CTY ROOM ON ALL UPPER LEVELS.

FLOOR PLAN LEGEND

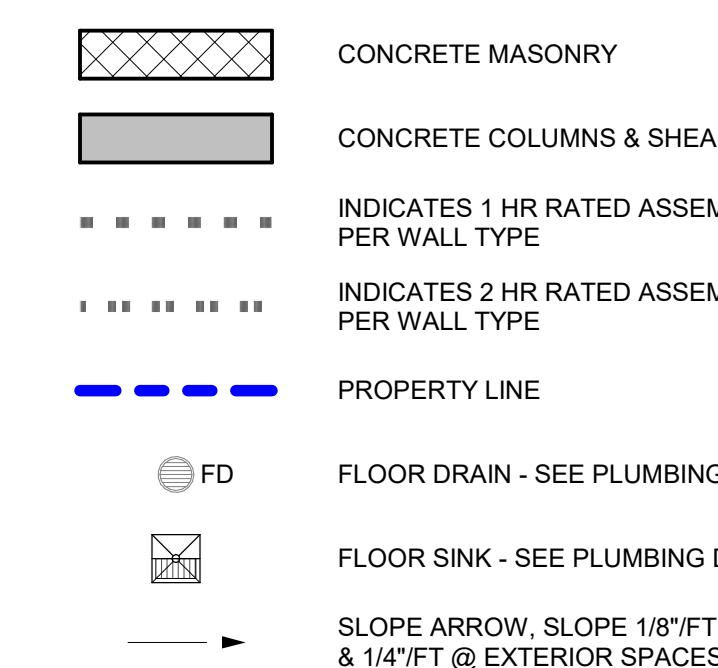


ELECTRICAL SYMBOLS

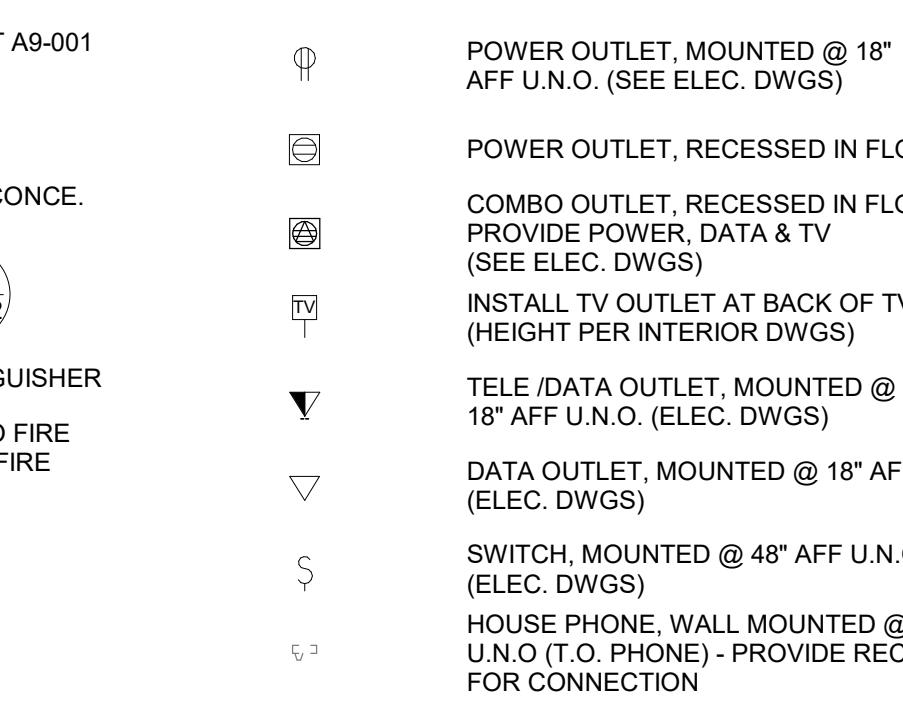

KEYNOTES / LEGENDS

KEYNOTE LEGEND

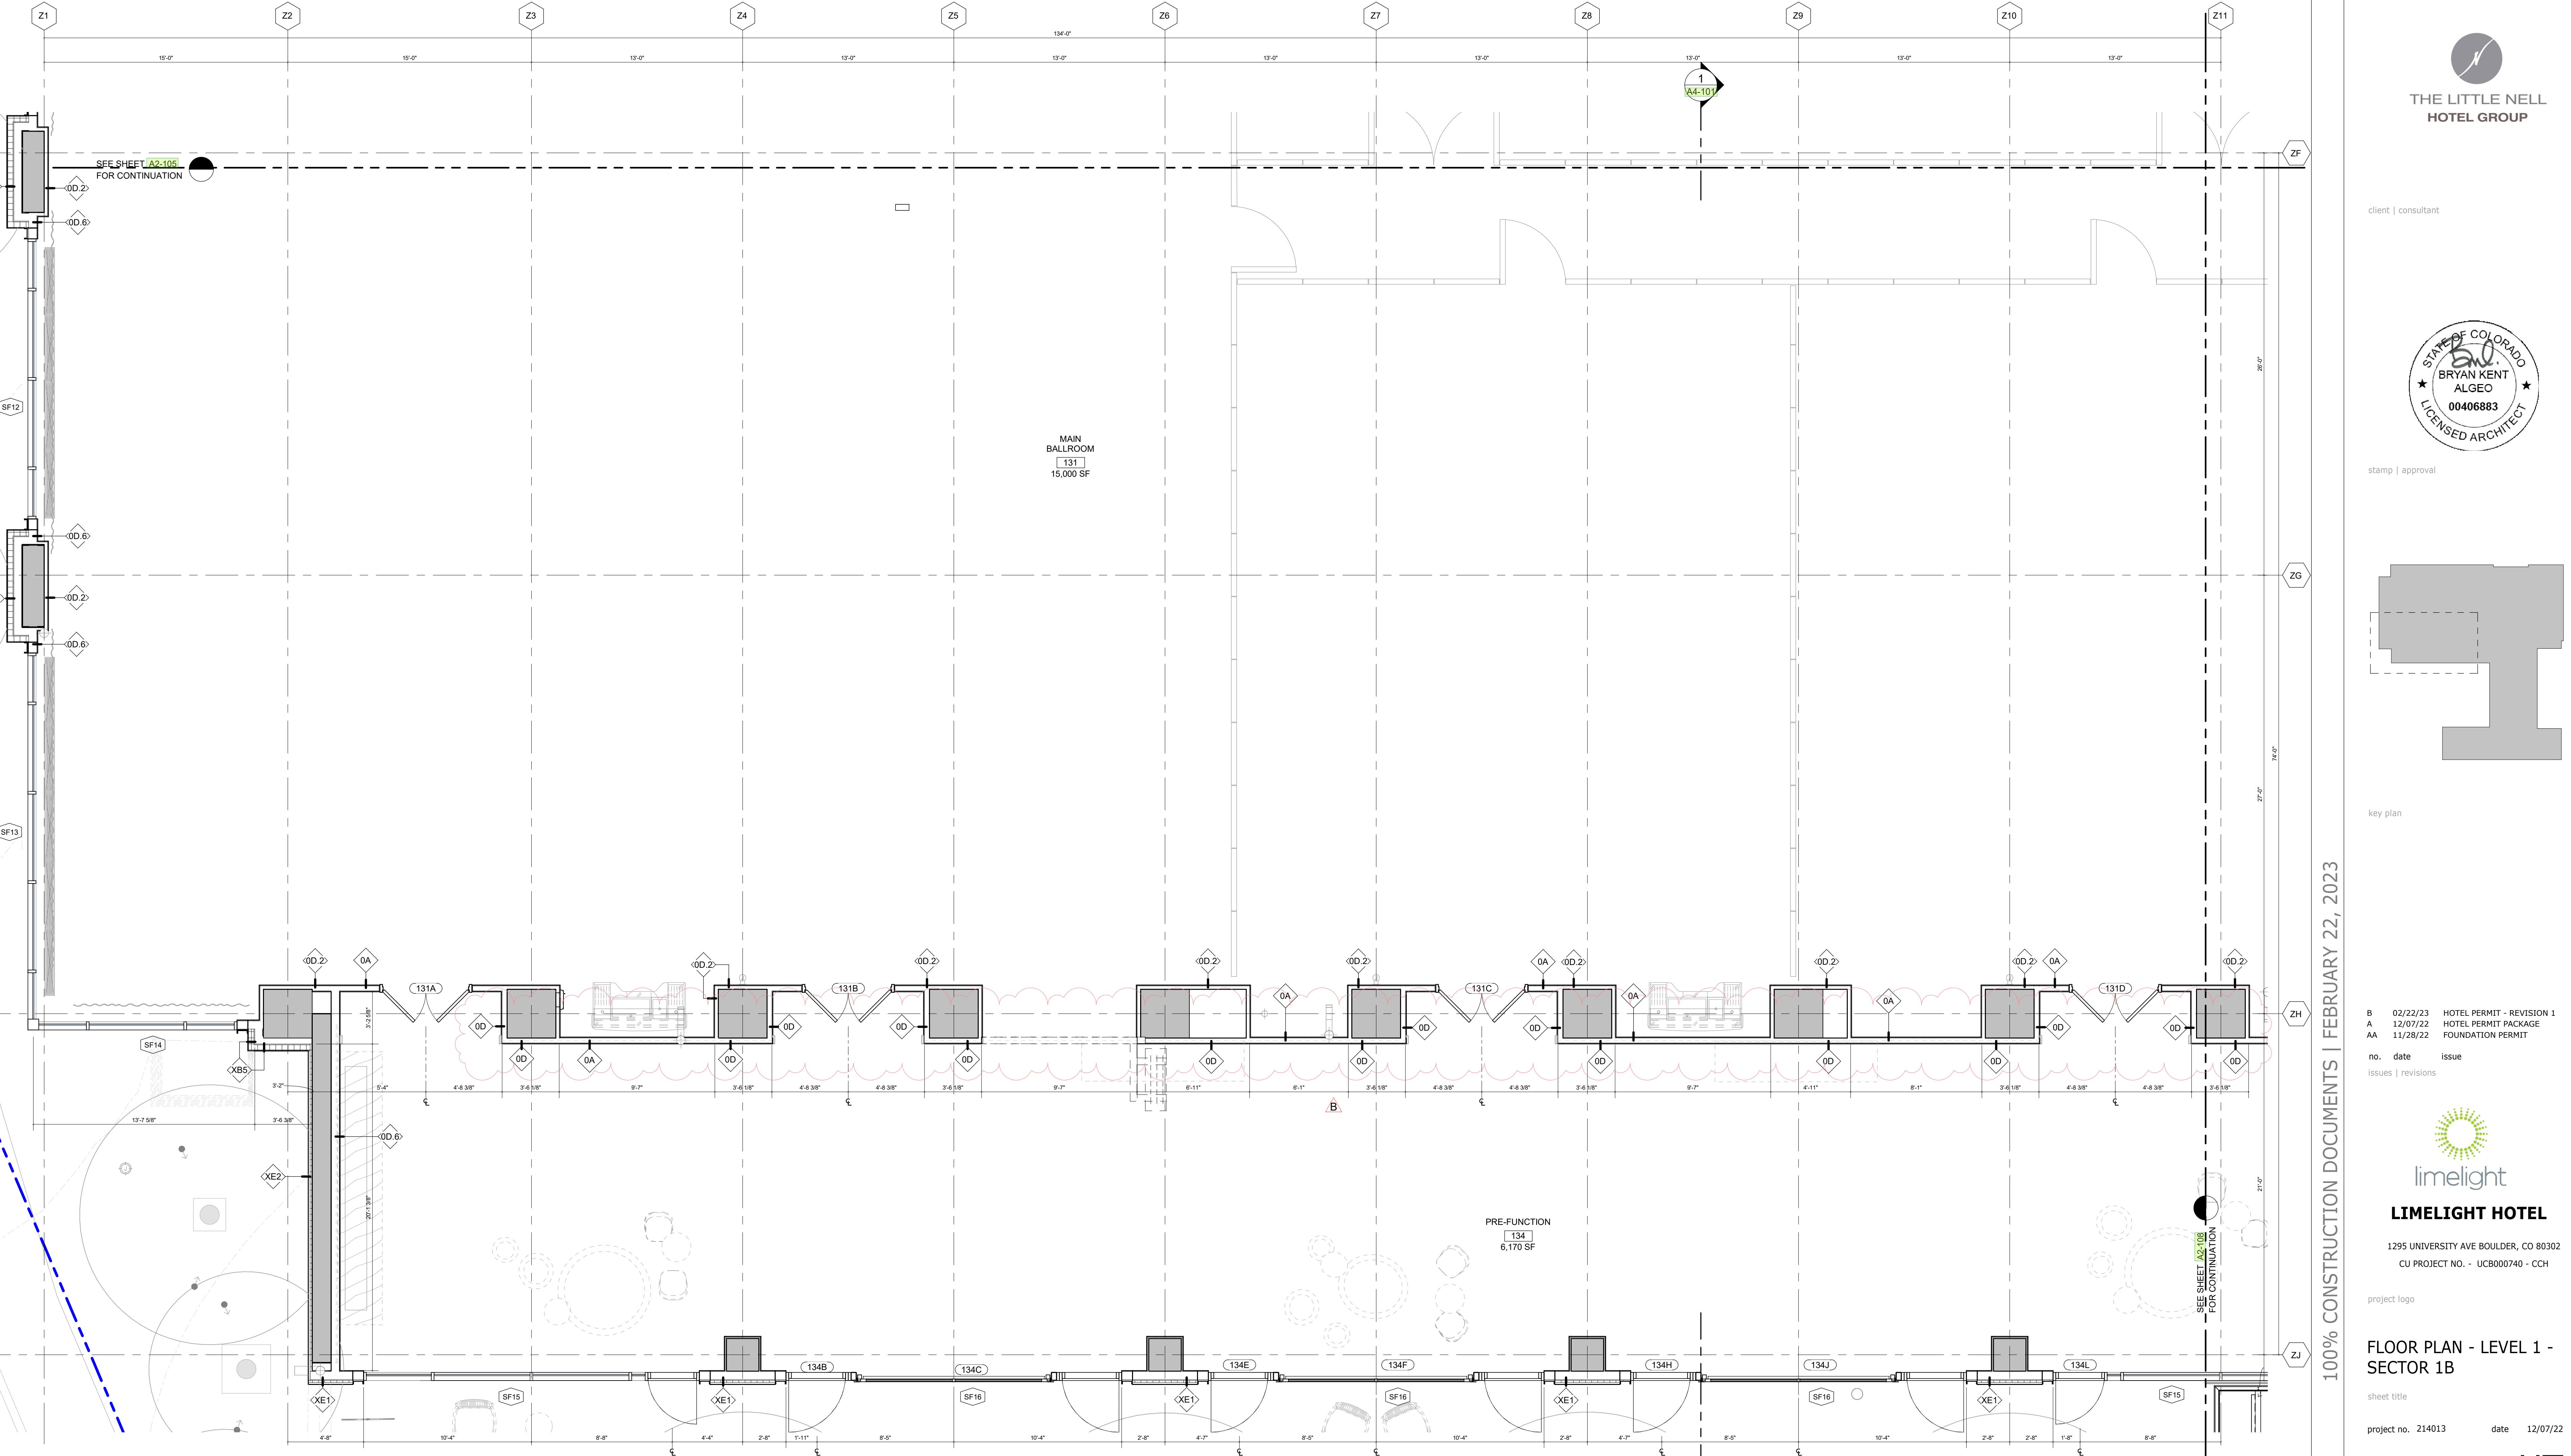

WATG

strategy planning architecture landscape interiors

irvine | CA | 949 574 8500

watg.com




THE LITTLE NELL
HOTEL GROUP

client | consultant



stamp | approval

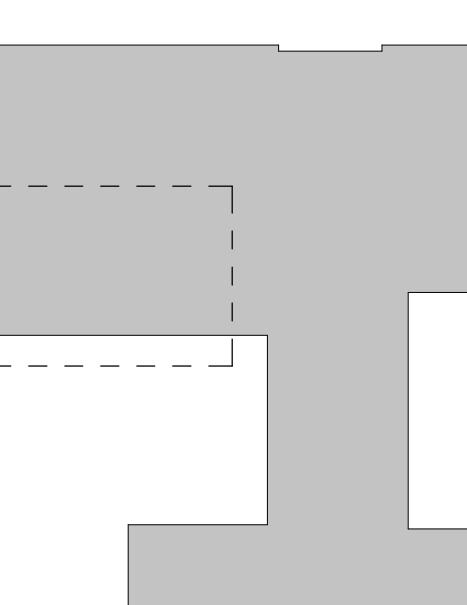

100% CONSTRUCTION DOCUMENTS | FEBRUARY 22, 2023

B 02/22/23 HOTEL PERMIT - REVISION 1
A 12/07/22 HOTEL PERMIT PACKAGE
AA 11/28/22 FOUNDATION PERMIT

no. date issue

issues | revisions



LIMELIGHT HOTEL

1295 UNIVERSITY AVE BOULDER, CO 80302
CU PROJECT NO. - UCB000740 - CCH

project logo

FLOOR PLAN - LEVEL 1 - SECTOR 1B


sheet title

project no. 214013

date 12/07/22

checked by: Checker

drawn by: Author

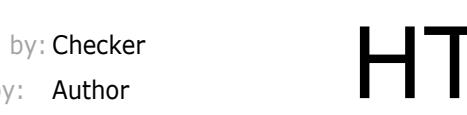

A2-106

sheet no.

FLOOR PLAN GENERAL NOTES

- ALL DIMENSIONS ARE TO THE FACE OF FINISH U.N.O.
- FOR UNIT PLANS SEE SHEETS A5-101 THROUGH A5-110
- FOR WALL PARTITION TYPES SEE SHEET A5-101
- FOR DOORS SEE SCHEDULES ON SHEET A10-101
- FOR WINDOWS & LOUVERS SEE SCHEDULES ON SHEET A10-101
- FOR BOH FINISHES SEE SHEET A10-01
- REFER TO SHEET A0-025 THROUGH A0-033 FOR ACCESSIBILITY REQUIREMENTS FOR ACCESS AND CLEARANCE
- WALL RATING LINES ARE INTENDED TO SHOW OCCUPANCY SEPARATIONS ONLY. REFER TO LIFE SAFETY CODE FOR REQUIRED RATINGS OF VARIOUS BUILDING ELEMENTS.
- ELEVATOR DOORS IN 2 HOUR SHAFT WALLS SHALL BE RATED 90 MINUTES
- CONDUIT FOR COUNTRYWIDE COORDINATED CONDUIT SYSTEM TO BE LOCATED IN CEILING. RUN CONDUIT VERTICALLY THROUGH CTY ROOM ON ALL UPPER LEVELS.

FLOOR PLAN LEGEND


	CONCRETE MASONRY
	CONCRETE COLUMNS & SHEAR WALLS
	INDICATES 1 HR RATED ASSEMBLY PER WALL TYPE
	INDICATES 2 HR RATED ASSEMBLY PER WALL TYPE
	PROPERTY LINE
	FLOOR DRAIN - SEE PLUMBING DWGS
	FLOOR SINK - SEE PLUMBING DWGS
	SLOPE ARROW, SLOPE 1/8" FT @ INTERIOR & 1/4" FT @ EXTERIOR SPACES U.N.O.

ELECTRICAL SYMBOLS

	POWER OUTLET, MOUNTED @ 18" AFF U.N.O. (SEE ELEC. DWGS)
	SIGNAGE KEYNOTE LEGEND
	WALL MOUNTED DECORATIVE SCONCE, PER INTERIOR DWGS
	SEMI-RECESSED FIRE EXTINGUISHER CABINET, A9-002
	STANDPIPE LOCATION, REFER TO FIRE SPRINKLER DWGS & APPROVED FIRE MASTER PLAN
	POWER OUTLET, RECESSED IN FLOOR, PROVIDE POWER, DATA & TV (SEE ELEC. DWGS)
	INSTALL TV OUTLET AT BACK OF TV. (HEIGHT PER INTERIOR DWGS)
	TELE/DATA OUTLET, MOUNTED @ 18" AFF U.N.O. (ELEC. DWGS)
	DATA OUTLET, MOUNTED @ 18" AFF U.N.O. (ELEC. DWGS)
	SWITCH, MOUNTED @ 48" AFF U.N.O. (ELEC. DWGS)
	HOUSE PHONE, WALL MOUNTED @ 48" AFF U.N.O. (T.O. PHONE) - PROVIDE RECEPTACLE FOR CONNECTION

KEYNOTES / LEGENDS

KEYNOTE LEGEND

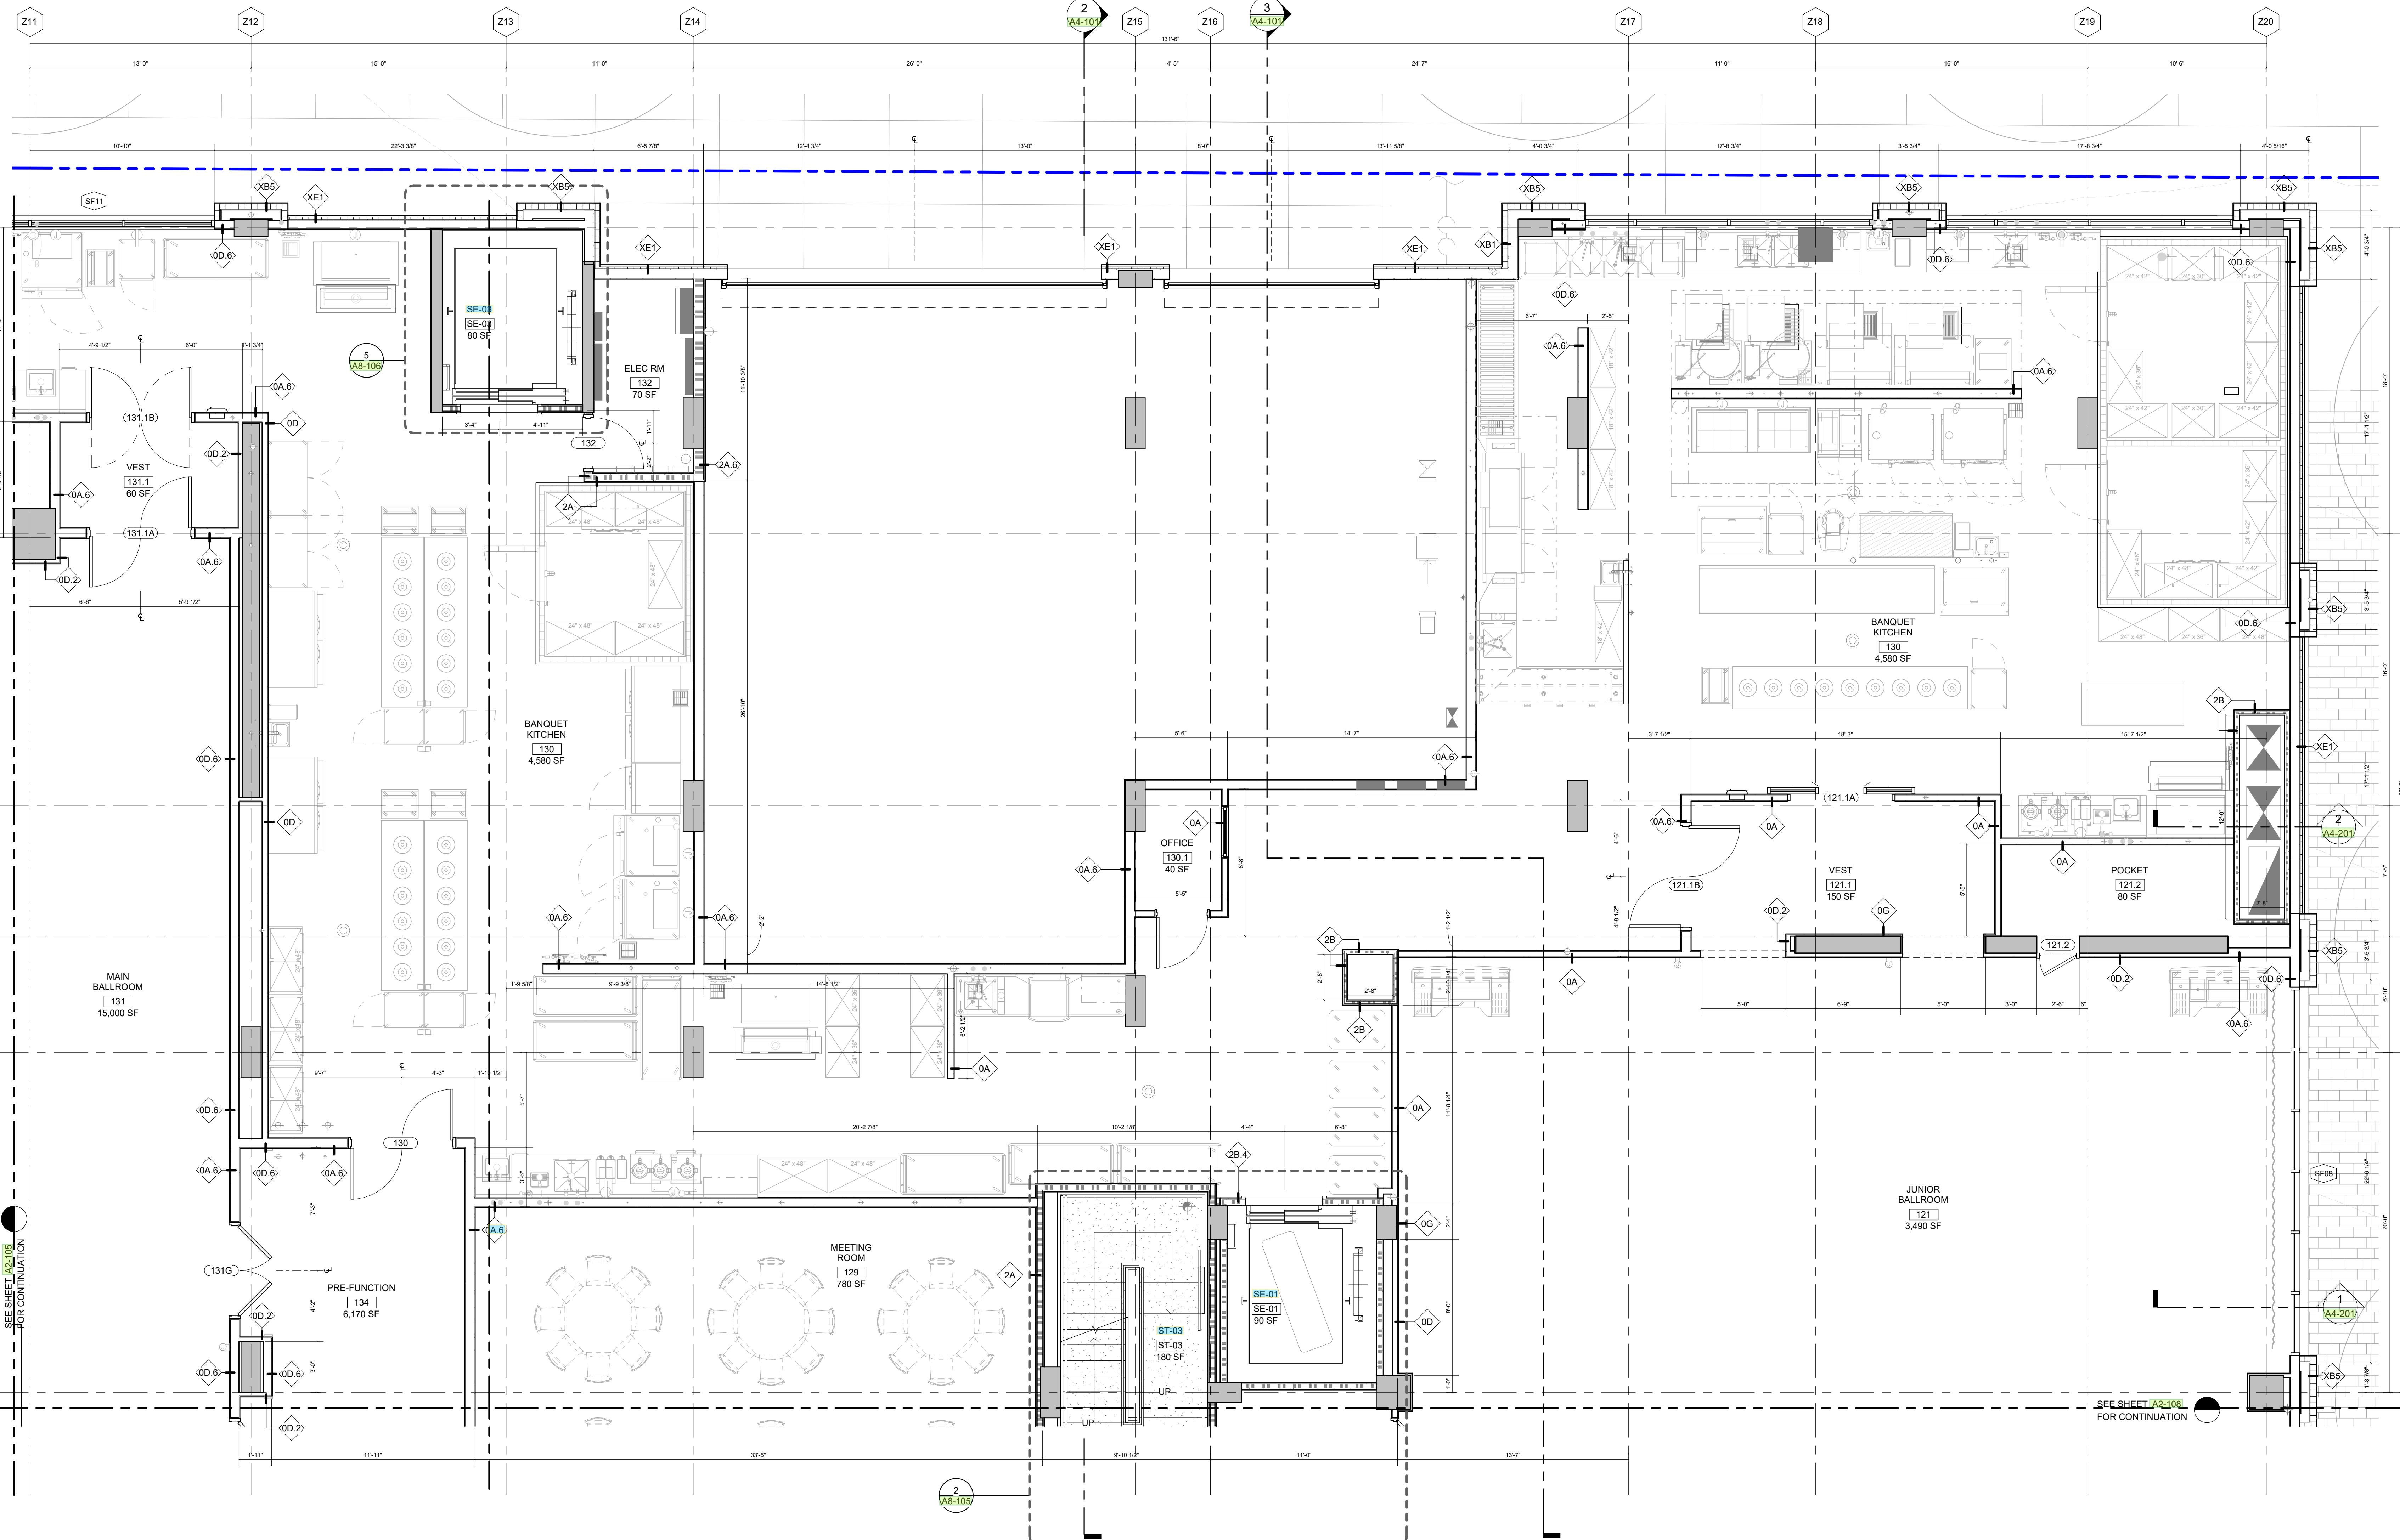

100% CONSTRUCTION DOCUMENTS | FEBRUARY 22, 2023

FLOOR PLAN - LEVEL 1 - SECTOR 2A

sheet title

project no. 214013

date 12/07/22

checked by: Checker

drawn by: Author

HT component

A2-107

WATG

strategy planning architecture landscape interiors

irvine | CA | 949 574 8500


watg.com



client | consultant



stamp | approval

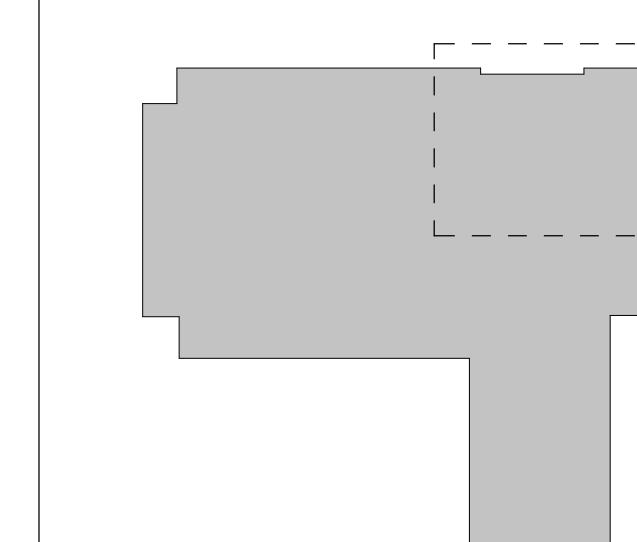

key plan


A 12/07/22 HOTEL PERMIT PACKAGE
AA 11/28/22 FOUNDATION PERMIT
no. date issue
issues | revisions



LIMELIGHT HOTEL

1295 UNIVERSITY AVE BOULDER, CO 80302
CU PROJECT NO. - UCB000740 - CCH

project logo

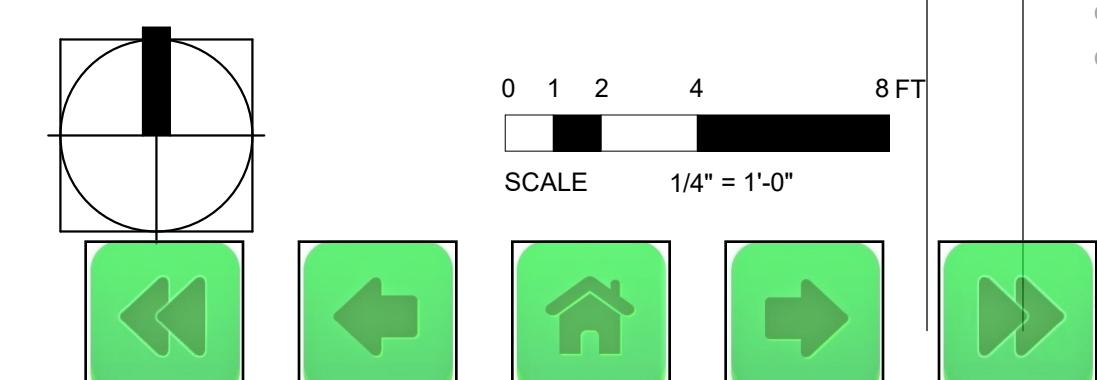

FLOOR PLAN GENERAL NOTES

- ALL DIMENSIONS ARE TO THE FACE OF FINISH U.N.O.
- FOR UNIT PLANS SEE SHEETS A5-101 THROUGH A5-110
- FOR WALL PARTITION TYPES SEE SHEET A5-101
- FOR DOORS SEE SCHEDULES ON SHEET A10-101
- FOR WINDOWS & LOUVERS SEE SCHEDULES ON SHEET A10-101
- FOR BOH FINISHES SEE SHEET A10-01
- REFER TO SHEET A025 THROUGH A033 FOR ACCESSIBILITY REQUIREMENTS FOR ACCESS AND CLEARANCE
- WALL RATING LINES ARE INTENDED TO SHOW OCCUPANCY SEPARATIONS ONLY. REFER TO LIFE SAFETY CODE FOR REQUIRED RATINGS OF VARIOUS BUILDING ELEMENTS.
- ELEVATORS IN 2 HOUR SHAFT WALLS SHALL BE RATED 90 MINUTES
- CONDUIT FOR COUNTRYWIDE COORDINATED CONDUIT SYSTEM TO BE LOCATED IN CEILING. RUN CONDUIT VERTICALLY THROUGH CTY ROOM ON ALL UPPER LEVELS.

FLOOR PLAN LEGEND

	CONCRETE MASONRY
	CONCRETE COLUMNS & SHEAR WALLS
	INDICATES 1 HR RATED ASSEMBLY PER WALL TYPE
	INDICATES 2 HR RATED ASSEMBLY PER WALL TYPE
	PROPERTY LINE
	FLOOR DRAIN - SEE PLUMBING DWGS
	FLOOR SINK - SEE PLUMBING DWGS
	SLOPE ARROW, SLOPE 1/8' FT @ INTERIOR & 1/4' FT @ EXTERIOR SPACES U.N.O.

ELECTRICAL SYMBOLS

	INTERIOR WALL TYPE PER SHEET A9-001
	SIGNAGE KEYNOTE LEGEND
	WALL MOUNTED DECORATIVE SCONCE, PER INTERIOR DWGS
	SEMI-RECESSED FIRE EXTINGUISHER CABINET, A9-002
	SURFACE MOUNTED FIRE EXTINGUISHER
	STANDPIPE LOCATION, REFER TO FIRE SPRINKLER DWGS & APPROVED FIRE MASTER PLAN
	POWER OUTLET, MOUNTED @ 18" AFF U.N.O. (SEE ELEC. DWGS)
	POWER OUTLET, RECESSED IN FLOOR
	COMBO OUTLET, RECESSED IN FLOOR, PROVIDE POWER, DATA & TV (SEE ELEC. DWGS)
	INSTALL TV OUTLET AT BACK OF TV. (HEIGHT FOR INTERIOR DWGS)
	DATA OUTLET, MOUNTED @ 18" AFF U.N.O. (ELEC. DWGS)
	SWITCH, MOUNTED @ 48" AFF U.N.O. (ELEC. DWGS)
	HOUSE PHONE, WALL MOUNTED @ 48" AFF U.N.O. (T.O. PHONE) - PROVIDE RECEPTACLE FOR CONNECTION

KEYNOTES / LEGENDS

KEYNOTE LEGEND	
S-1	TACTILE SIGNAGE - "EXIT" SEE DTL 19/A0-020
S-6	TAKEABLE FLOOR LEVEL IDENTIFICATION SIGNAGE, MOUNT AT 60" AFF TO CENTERLINE OF SIGNAGE
S-13	STARWELL IDENTIFICATION SIGNAGE PER DTL 24/A0-020

WATG

strategy planning architecture landscape interiors

irvine | CA | 949 574 8500


watg.com



client | consultant



stamp | approval

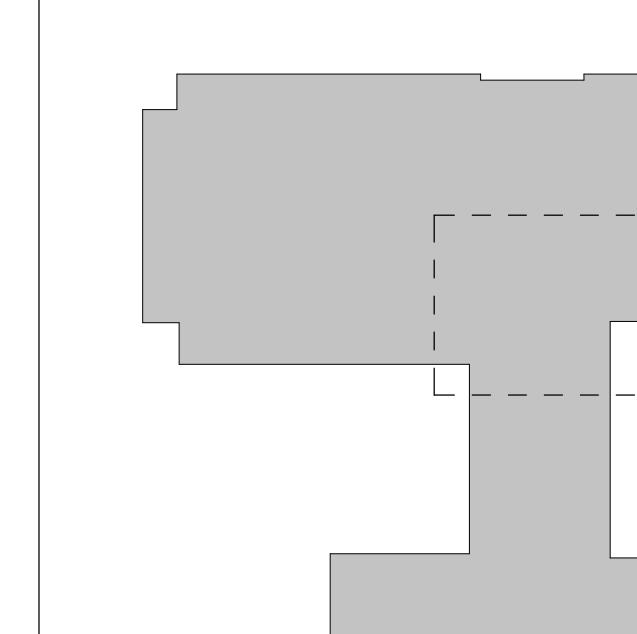

key plan



LIMELIGHT HOTEL

1295 UNIVERSITY AVE BOULDER, CO 80302
CU PROJECT NO. - UCB000740 - CCH

project logo

100% CONSTRUCTION DOCUMENTS | FEBRUARY 22, 2023

B 02/22/23 HOTEL PERMIT - REVISION 1
A 12/07/22 HOTEL PERMIT PACKAGE
AA 11/28/22 FOUNDATION PERMIT

no. date issue

issues | revisions



limelight

LIMELIGHT HOTEL

1295 UNIVERSITY AVE BOULDER, CO 80302
CU PROJECT NO. - UCB000740 - CCH

project logo

FLOOR PLAN - LEVEL 1 - SECTOR 2B

sheet title

project no. 214013

date 12/07/22

checked by: Checker

drawn by: Author

scale 0 1 2 4 8 FT

SCALE 1/4" = 1'-0"


sheet no.

A2-108


FLOOR PLAN GENERAL NOTES

1. ALL DIMENSIONS ARE TO THE FACE OF FINISH U.N.O.
2. FOR UNIT PLANS SEE SHEETS A5-101 THROUGH A5-110
3. FOR WALL PARTITION TYPES SEE SHEET A5-101
4. FOR DOORS SEE SCHEDULES ON SHEET A10-101
5. FOR WINDOWS & LOUVERS SEE SCHEDULES ON SHEET A10-101
6. FOR BOH FINISHES SEE SHEET A10-01
7. REFER TO SHEET A0-025 THROUGH A0-033 FOR ACCESSIBILITY REQUIREMENTS FOR ACCESS AND CLEARANCES
8. WALL RATING LINES ARE INTENDED TO SHOW OCCUPANCY SEPARATIONS ONLY. REFER TO LIFE SAFETY CODE FOR REQUIRED RATINGS OF VARIOUS BUILDING ELEMENTS
9. ELEVATOR DOORS IN 2 HOUR SHAFT WALLS SHALL BE RATED 90 MINUTES
10. CONDUIT FOR COUNTRYWIDE COORDINATED CONDUIT SYSTEM TO BE LOCATED IN CEILING. RUN CONDUIT VERTICALLY THROUGH CTY ROOM ON ALL UPPER LEVELS.

FLOOR PLAN LEGEND

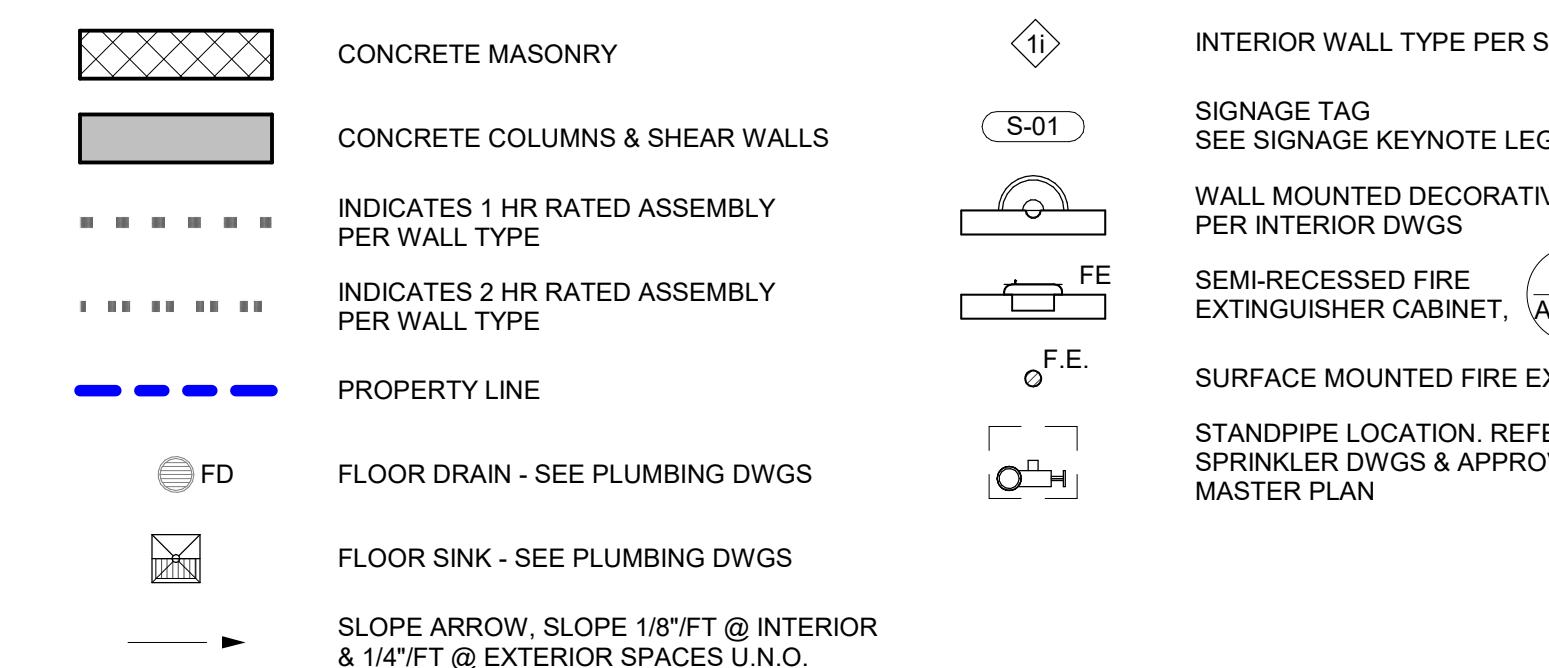


ELECTRICAL SYMBOLS

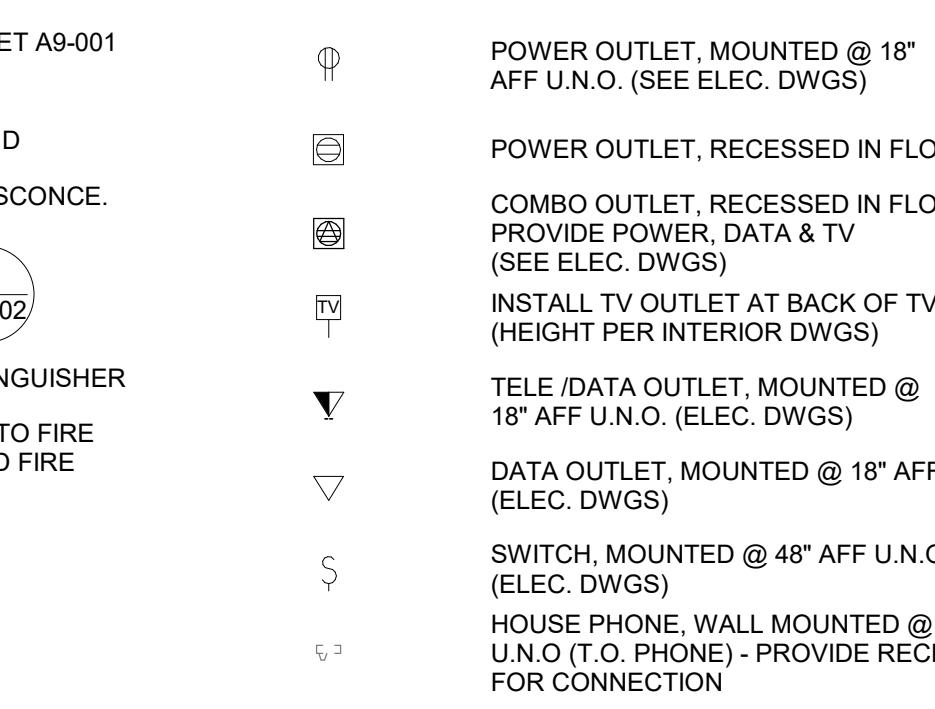

KEYNOTES / LEGENDS


KEYNOTE LEGEND

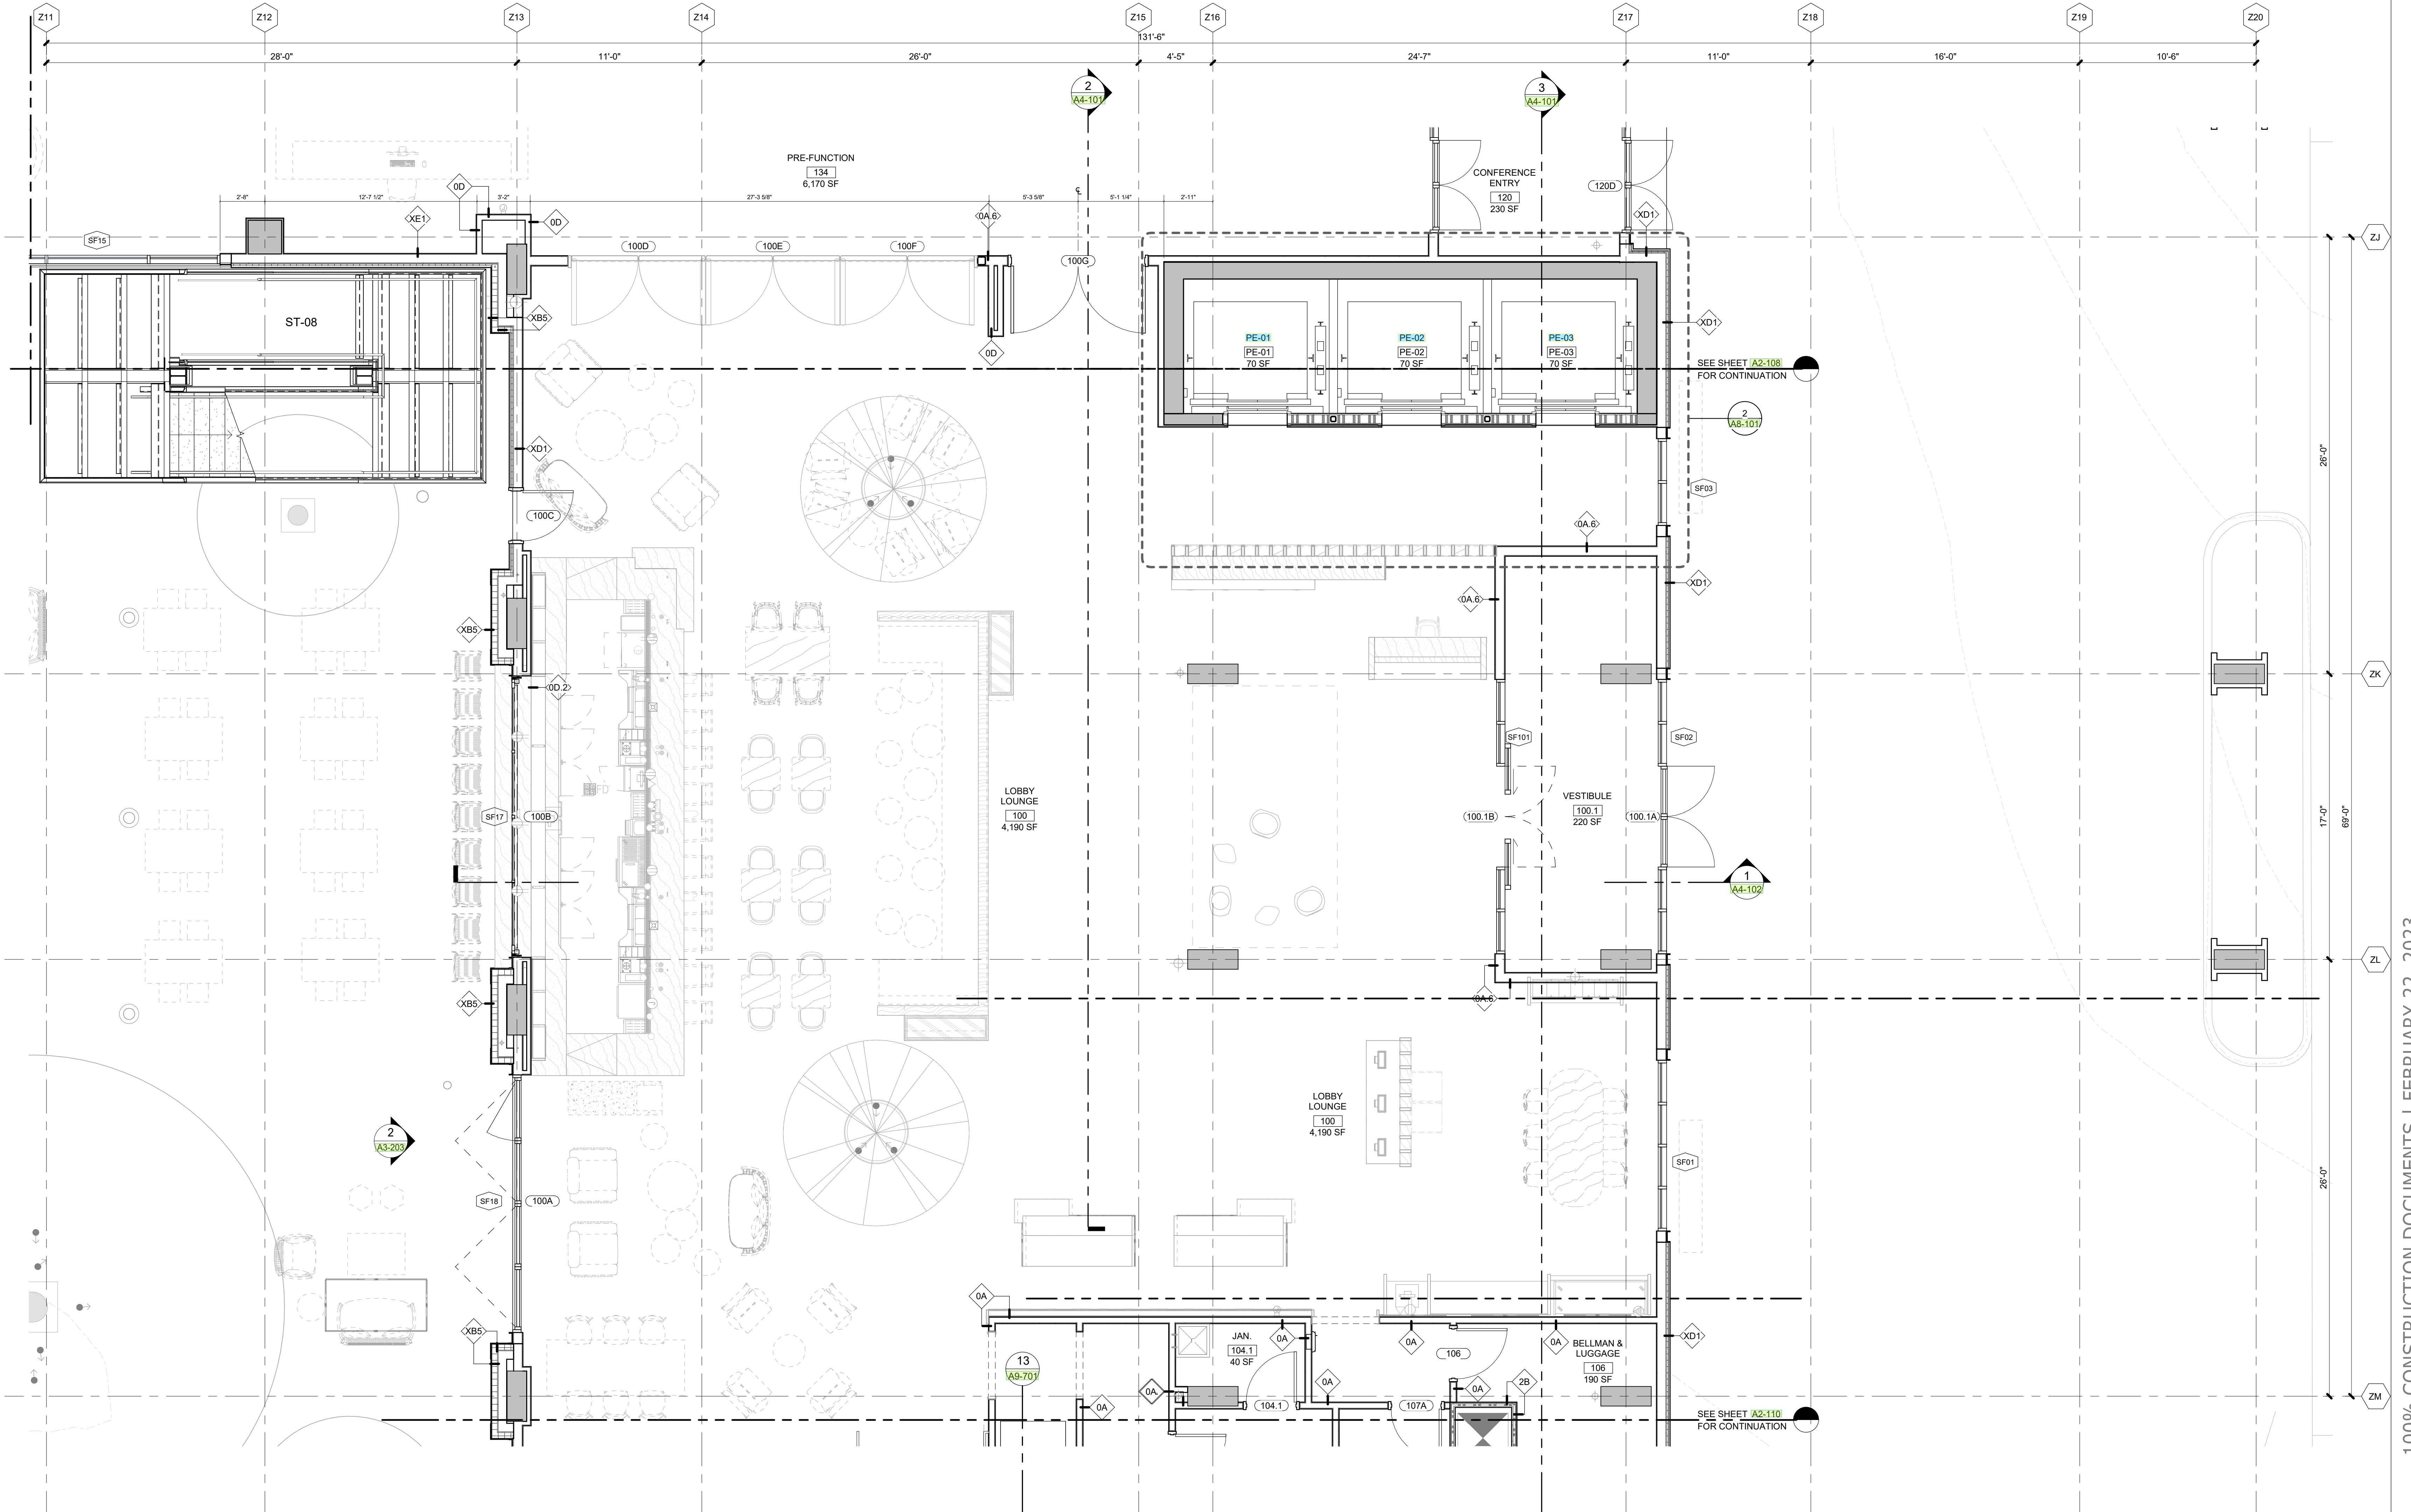


FLOOR PLAN GENERAL NOTES

1. ALL DIMENSIONS ARE TO THE FACE OF FINISH U.N.O.
 2. FOR UNIT PLANS SEE SHEETS A5-101 THROUGH A5-110
 3. FOR WALL PARTITION TYPES SEE SHEET A9-101
 4. FOR DOORS SEE SCHEDULES ON SHEET A10-101
 5. FOR WINDOWS & LOUVERS SEE SCHEDULES ON SHEET A10-106
 6. FOR BOH FINISHES SEE SHEET A10-01
 7. REFER TO SHEET A0-025 THROUGH A0-033 FOR ACCESSIBILITY REQUIREMENTS FOR ACCESS AND CLEARANCE.
 8. WALL RATING LINES ARE INTENDED TO SHOW OCCUPANCY SEPARATIONS ONLY. REFER TO LIFE SAFETY DWGS FOR REQUIRED RATINGS OF VARIOUS BUILDING ELEMENTS.
 9. ELEVATOR DOORS IN 2 HOUR SHAFT WALLS SHALL BE RATED 90 MINUTES
 10. CONDUIT FOR COUNTRYWIDE COORDINATED COMMUNICATION SYSTEM TO BE LOCATED IN CEILING. RUN CONDUIT VERTICALLY THROUGH CTV ROOM ON ALL UPPER LEVELS.
 11. PER IBC 1022.5 AND 1023.5, PLUMBING, DUCTS, AND CONDUITS SHALL NOT BE LOCATED IN STAIR ENCLOSURE OR EXIT PASSAGEWAY.
 12. CONTINUOUS INSULATION AT OUTSIDE OF EXTERIOR METAL STUD WALL. REFER TO WALL DETAILS AND SPECIFICATIONS.
 13. PROVIDE BACKING AT ALL ARTWORK, MIRRORS, ETC. AS REQUIRED.
 14. MOUNT TV ON FURNITURE IF REQUIRED. TO BE MOUNTED ON WALL, USE BACKING PER DETAIL A9-102 /10
 15. REFER TO INTERIOR DWGS FOR ALL ELECTRICAL, DATA & CONTROL LOCATIONS

FLOOR PLAN

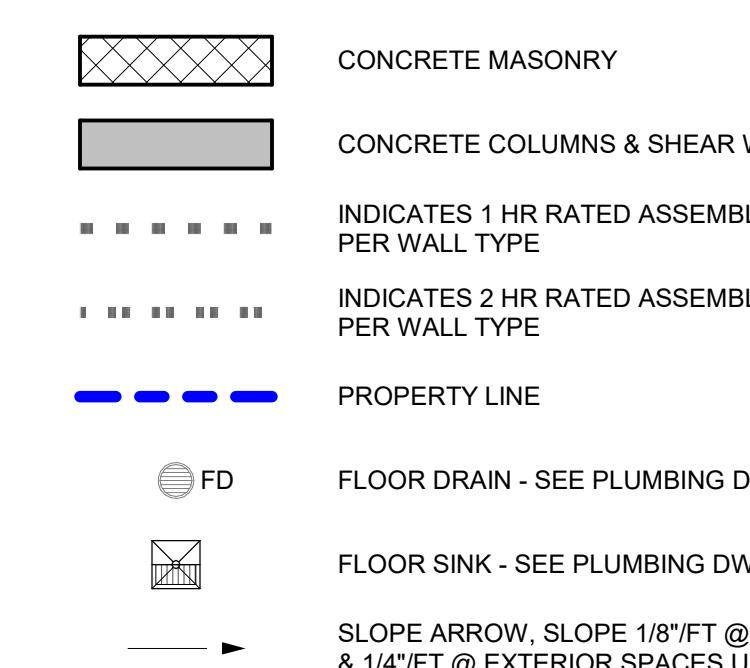

ELECTRICAL SYMB

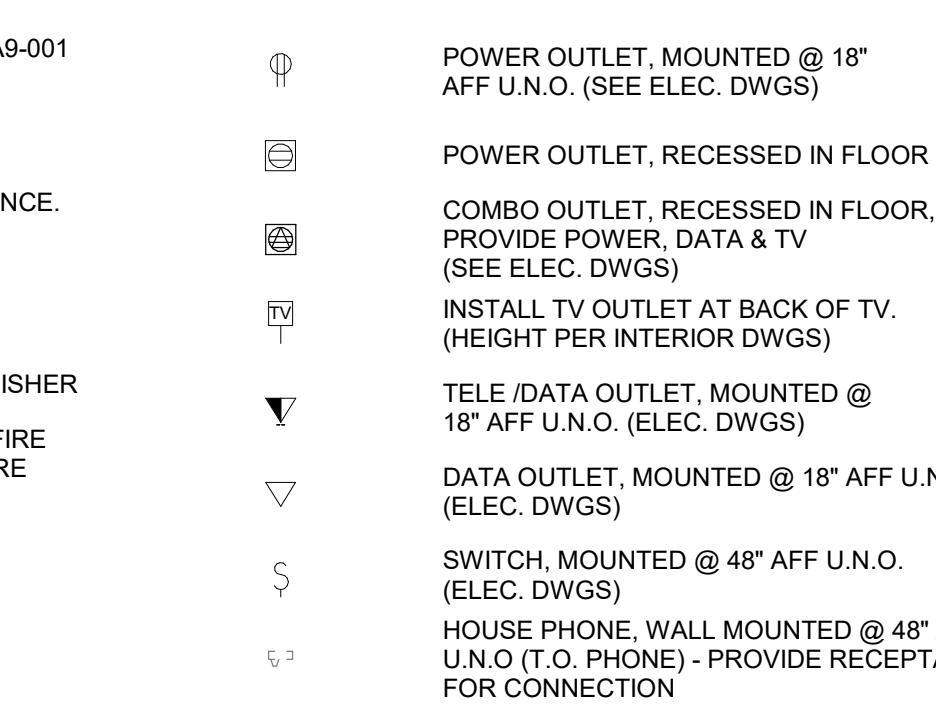

KEYNOTES / LEGENDS

KEYNOTE LEGEND

WATG

strategy planning architecture landscape interiors

irvine | CA | 949 574 8500 watc

tg.com




THE LITTLE NELL HOTEL GROUP

client | consu



stamp | a

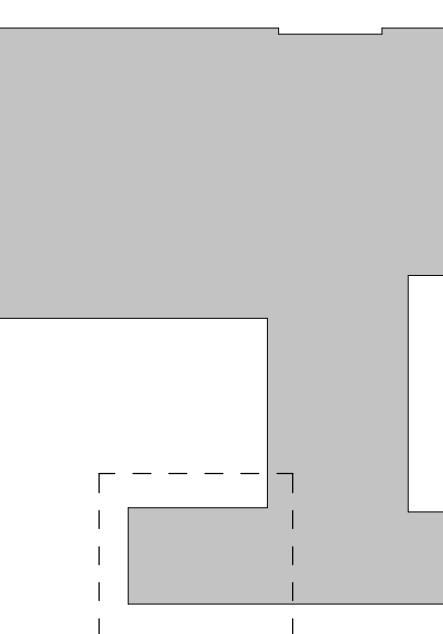

100% CONSTRUCTION DOCUMENTS | FEBRUARY 22, 2023

A	12/07/22	HOTEL PERMIT PACKAGE
AA	11/28/22	FOUNDATION PERMIT
no.	date	issue

2

FLOOR PLAN - LEVEL 1 -
SECTOR 5

sheet title

project no. 214013 date 12/0

HT
component

A2-111

2/22/2023 6:27:26 PM
The original size of this drawing is 30" x 42"
Copyright © 2016 WAIS All rights reserved

2/22/2023 6:27:26 PM
The original size of this drawing is 30"x42"

1 FLOOR PLAN - LEVEL 1 - SECTOR 5

1/4" = 1'-0"

■ $1/4 = 1 - 0$

The image shows an architectural drawing of a circle with a vertical line through its center. Below the drawing are four green arrows pointing left, right, up, and down. To the right of the drawing is a scale bar with markings at 0, 1, 2, 4, and 8 FT. The text "SCALE 1/4\" data-bbox="510 380 790 410" data-label="Text"/> = 1'-0" is also present.

sheet no.